



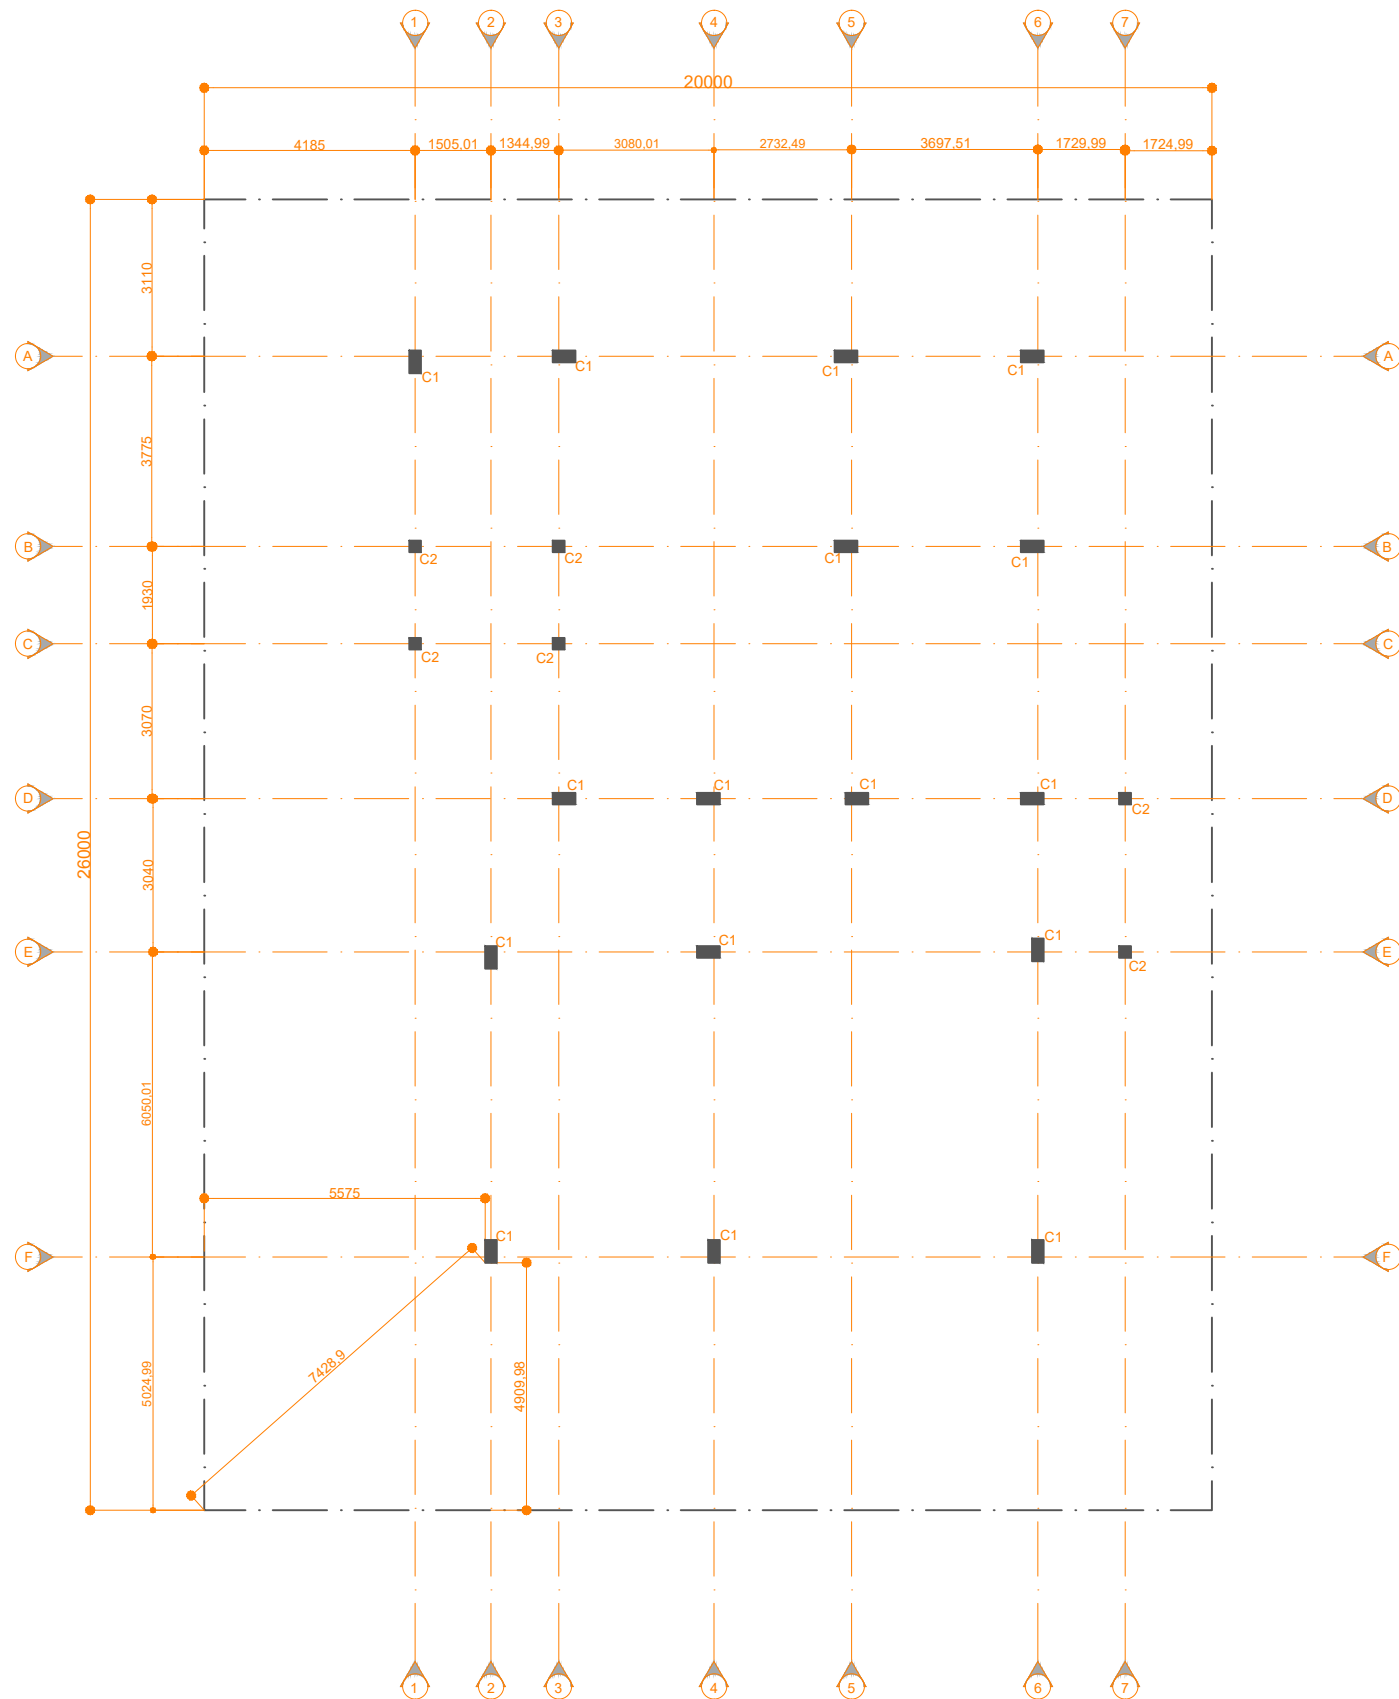

SETTING OUT PLAN

KEY PLAN

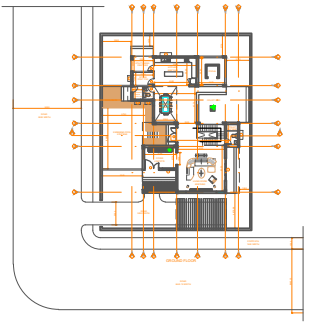

Notes:
1.While every attempt has been made in preparation of this drawing to avoid mistakes, the maker cannot guarantee against human error. The contractor on the job must check all dimensions and other details and be responsible for the same.
2.Unless otherwise mentioned all dimensions are in mm.
3.Written dimensions to be followed. Do not scale any measurement from the drawings.
4.Any discrepancy in this or any other drawings related to this drawing shall be brought to the notice of architects immediately.
5.This drawing is to be read in conjunction with related structural and services drawing.


IMPORTANT NOTE:

THIS IS THE PROPERTY OF ARTHA-R ARCHITECTS GROUP & IS NOT TO BE COPIED, ISSUED, OR LOANED TO ANY THIRD PARTY FOR ANY PURPOSE OTHER THAN FOR WHICH IT HAS BEEN ISSUED.




DRAWING NAME: SETTING OUT PLAN

PROJECT TITLE:	VILLA HOUSE		
CLIENT NAME:	MS		
LOCATION:			
PLOT NO:		BLOCK NO:	
DESIGN BY:	KARAN	PROJECT NO:	
DRAWN BY:	KARAN	SHEET NO:	
CHECKED BY:		SCALE:	1:150
DRAWING NAME:	AR-01-ST-001-R00		

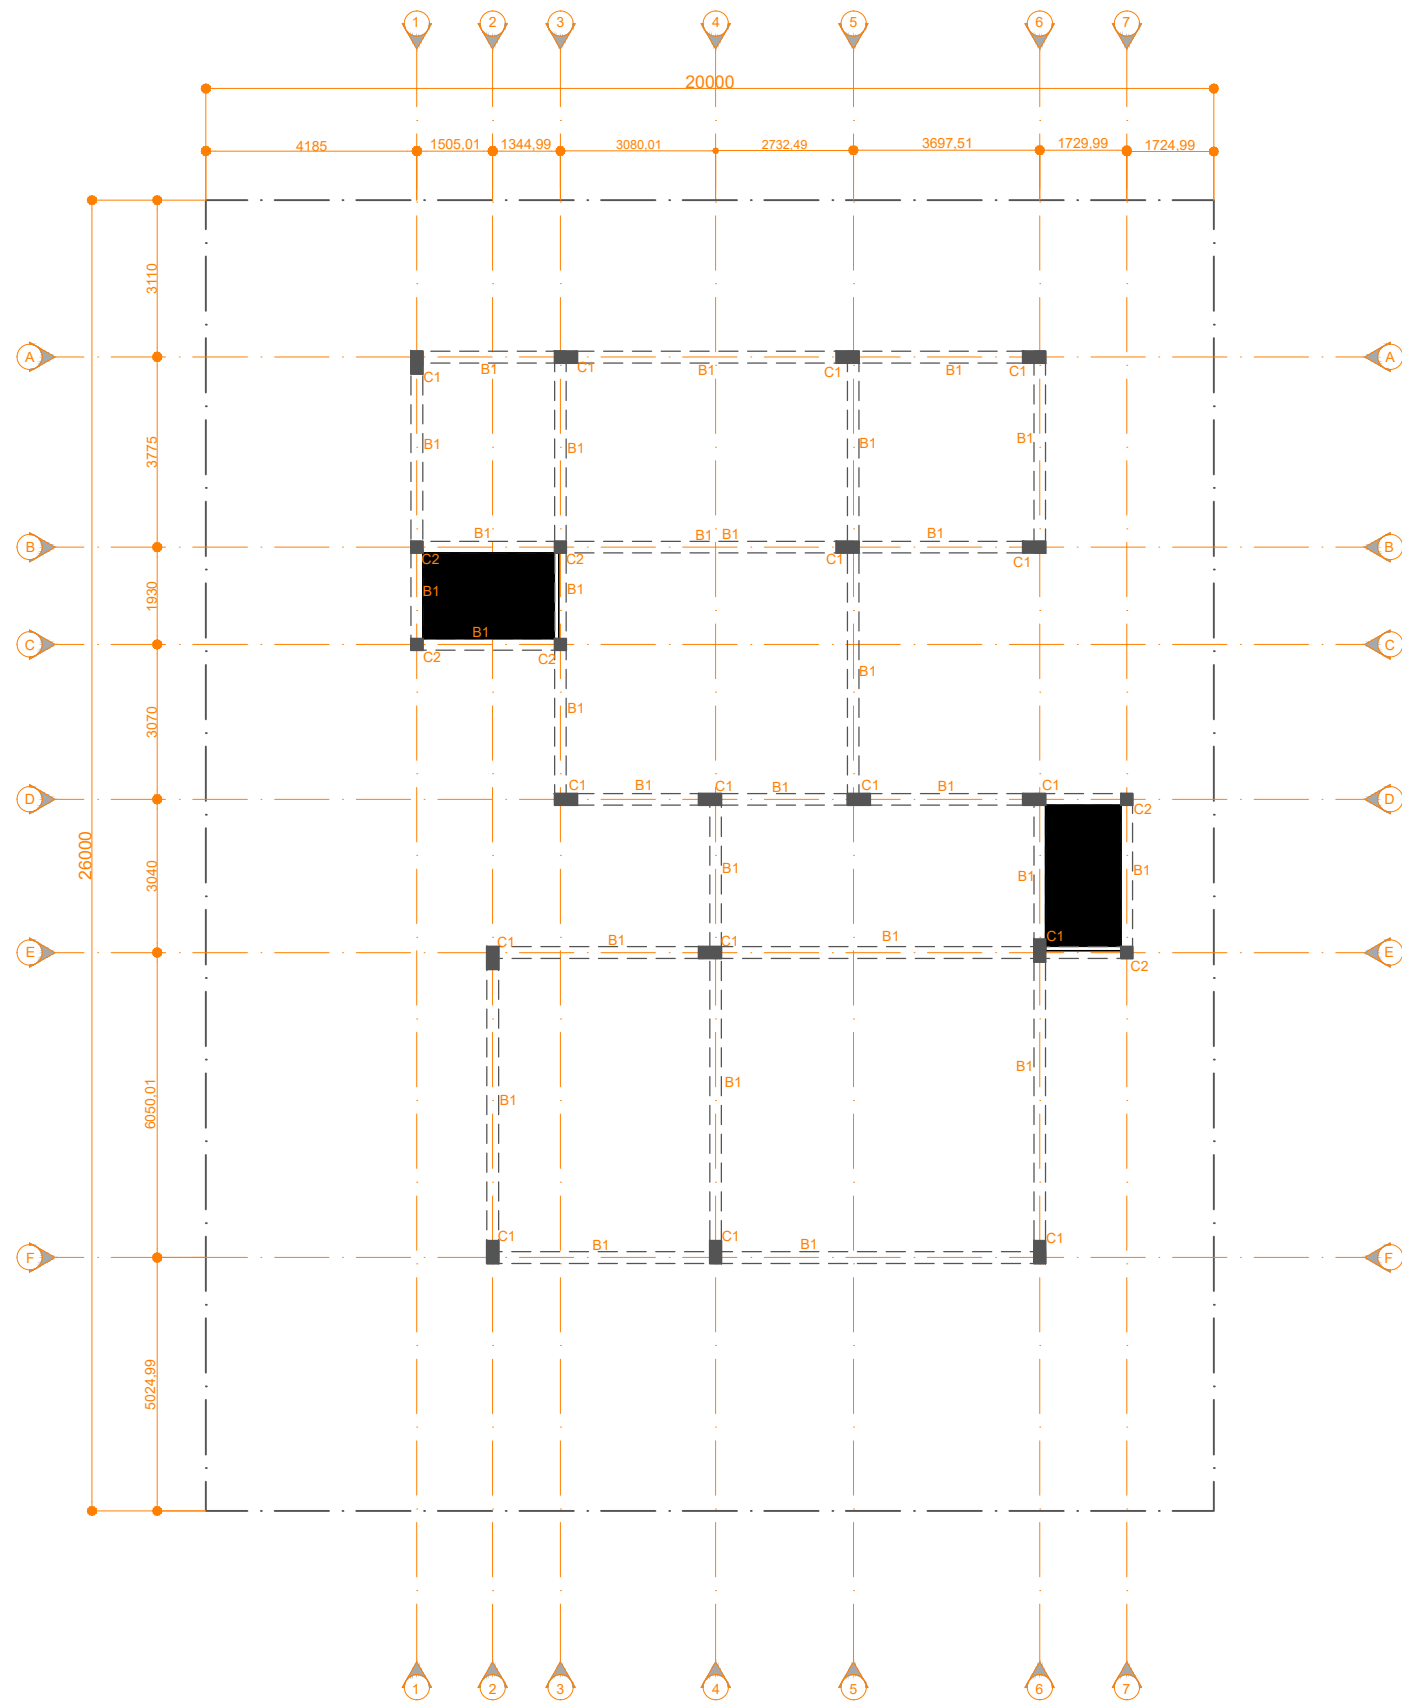

PLINTH BEAM PLAN

KEY PLAN

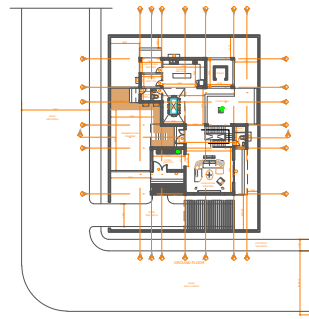

Notes:
1.While every attempt has been made in preparation of this drawing to avoid mistakes, the maker cannot guarantee against human error. The contractor on the job must check all dimensions and other details and be responsible for the same.
2.Unless otherwise mentioned all dimensions are in mm.
3.Written dimensions to be followed. Do not scale any measurement from the drawings.
4.Any discrepancy in this or any other drawings related to this drawing shall be brought to the notice of architects immediately.
5.This drawing is to be read in conjunction with related structural and services drawing.


IMPORTANT NOTE:

THIS IS THE PROPERTY OF ARTHA-R ARCHITECTS GROUP & IS NOT TO BE COPIED, ISSUED, OR LOANED TO ANY THIRD PARTY FOR ANY PURPOSE OTHER THAN FOR WHICH IT HAS BEEN ISSUED.




DRAWING NAME: PLINTH BEAM PLAN

PROJECT TITLE:	VILLA HOUSE		
CLIENT NAME:	MS		
LOCATION:			
PLOT NO:		BLOCK NO:	
DESIGN BY:	KARAN	PROJECT NO:	
DRAWN BY:	KARAN	SHEET NO:	
CHECKED BY:		SCALE:	1:150
DRAWING NAME:	AR-01-ST-003-R00		

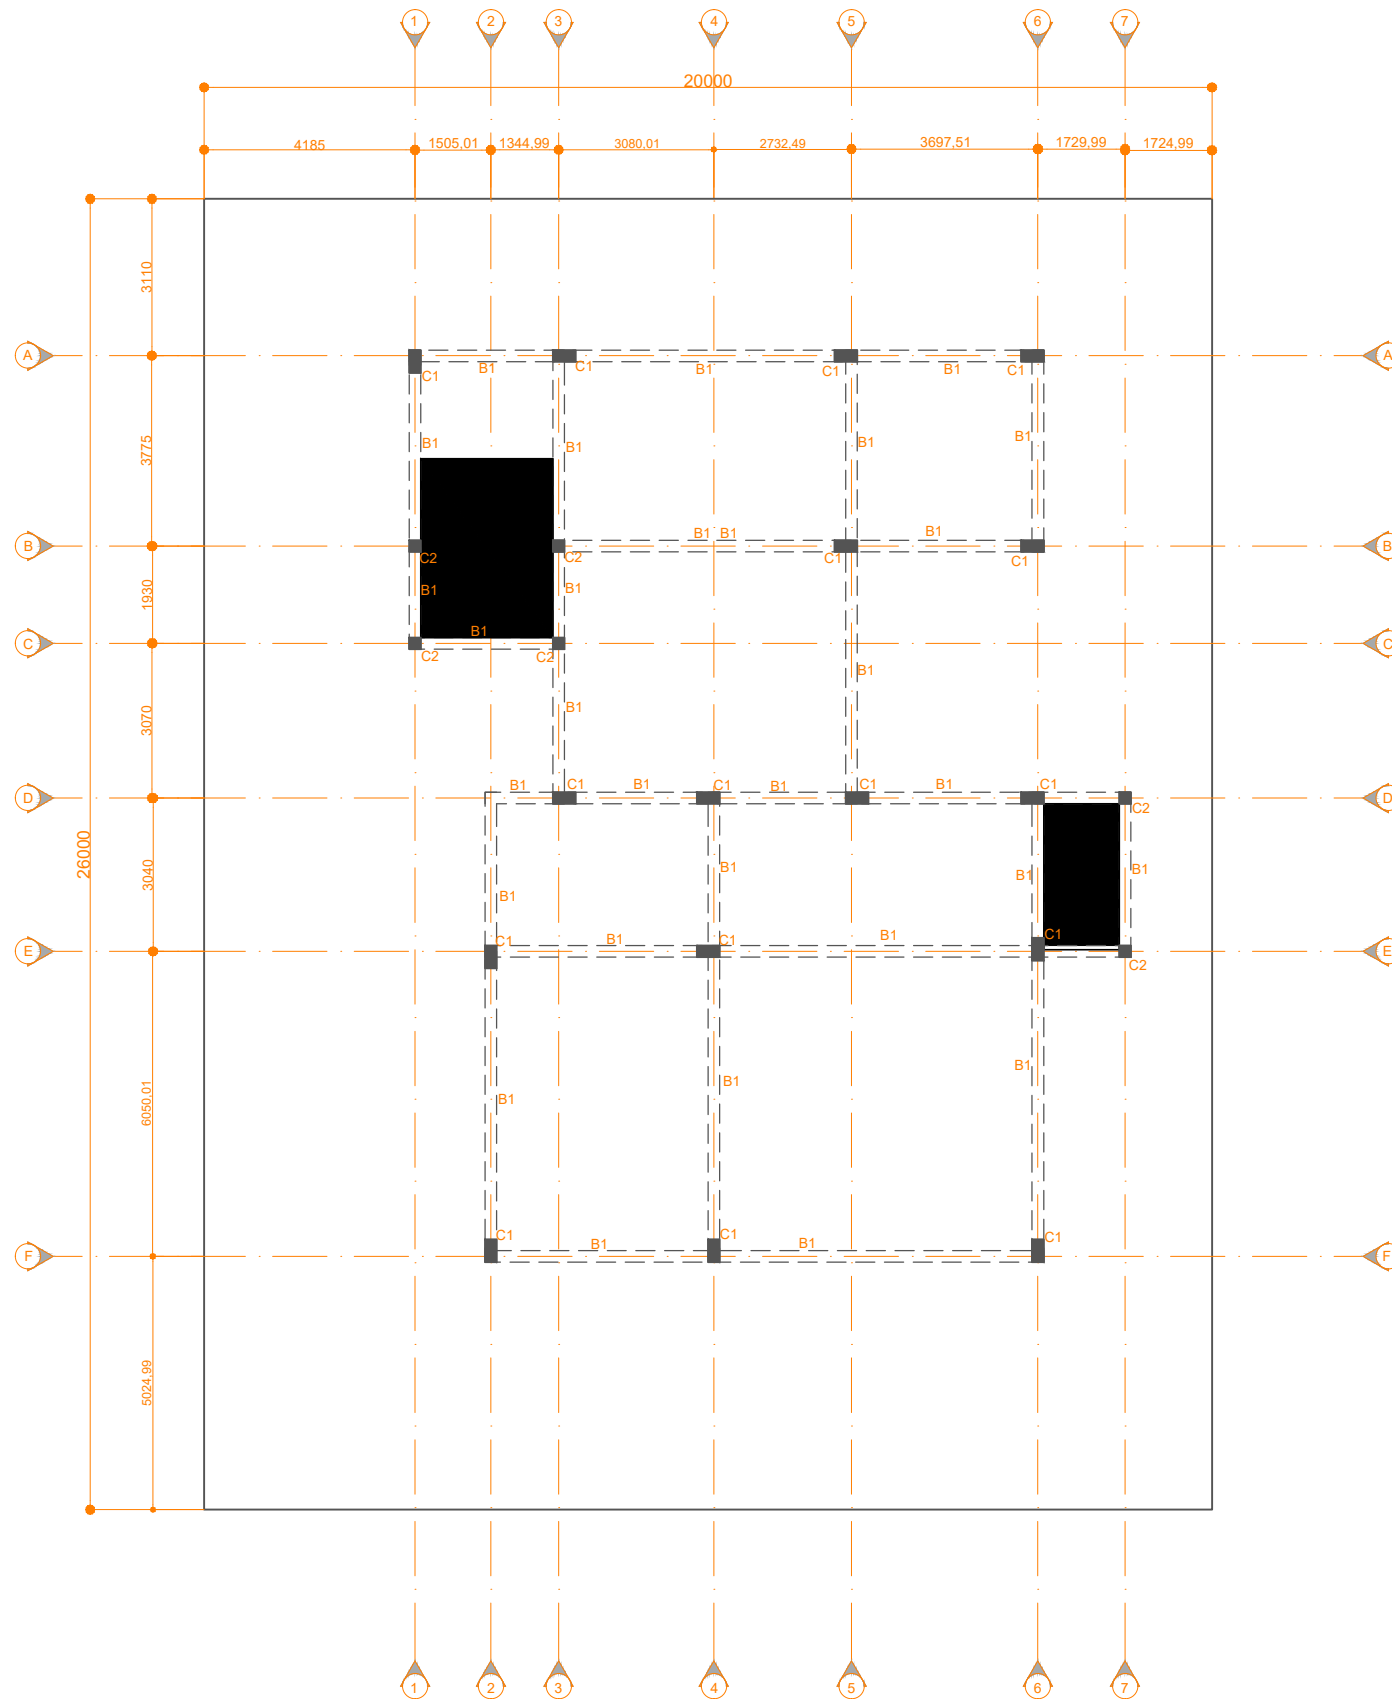

FIRST FLOOR BEAM PLAN

KEY PLAN

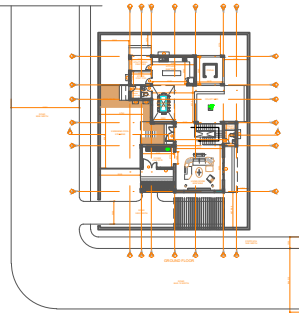

Notes:
1.While every attempt has been made in preparation of this drawing to avoid mistakes, the maker cannot guarantee against human error. The contractor on the job must check all dimensions and other details and be responsible for the same.
2.Unless otherwise mentioned all dimensions are in mm.
3.Written dimensions to be followed. Do not scale any measurement from the drawings.
4.Any discrepancy in this or any other drawings related to this drawing shall be brought to the notice of architects immediately.
5.This drawing is to be read in conjunction with related structural and services drawing.

IMPORTANT NOTE:

THIS IS THE PROPERTY OF ARTHAR ARCHITECTS GROUP & IS NOT TO BE COPIED, ISSUED, OR LOANED TO ANY THIRD PARTY FOR ANY PURPOSE OTHER THAN FOR WHICH IT HAS BEEN ISSUED.



DRAWING NAME: FIRST FLOOR BEAM PLAN

PROJECT TITLE: VILLA HOUSE

CLIENT NAME: MS

LOCATION:

PLOT NO:

BLOCK NO:

DESIGN BY:

KARAN

PROJECT NO:

DRAWN BY:

KARAN

SHEET NO:


CHECKED BY:

SCALE:


1:150

DRAWING NAME:

AR-01-ST-004-R00

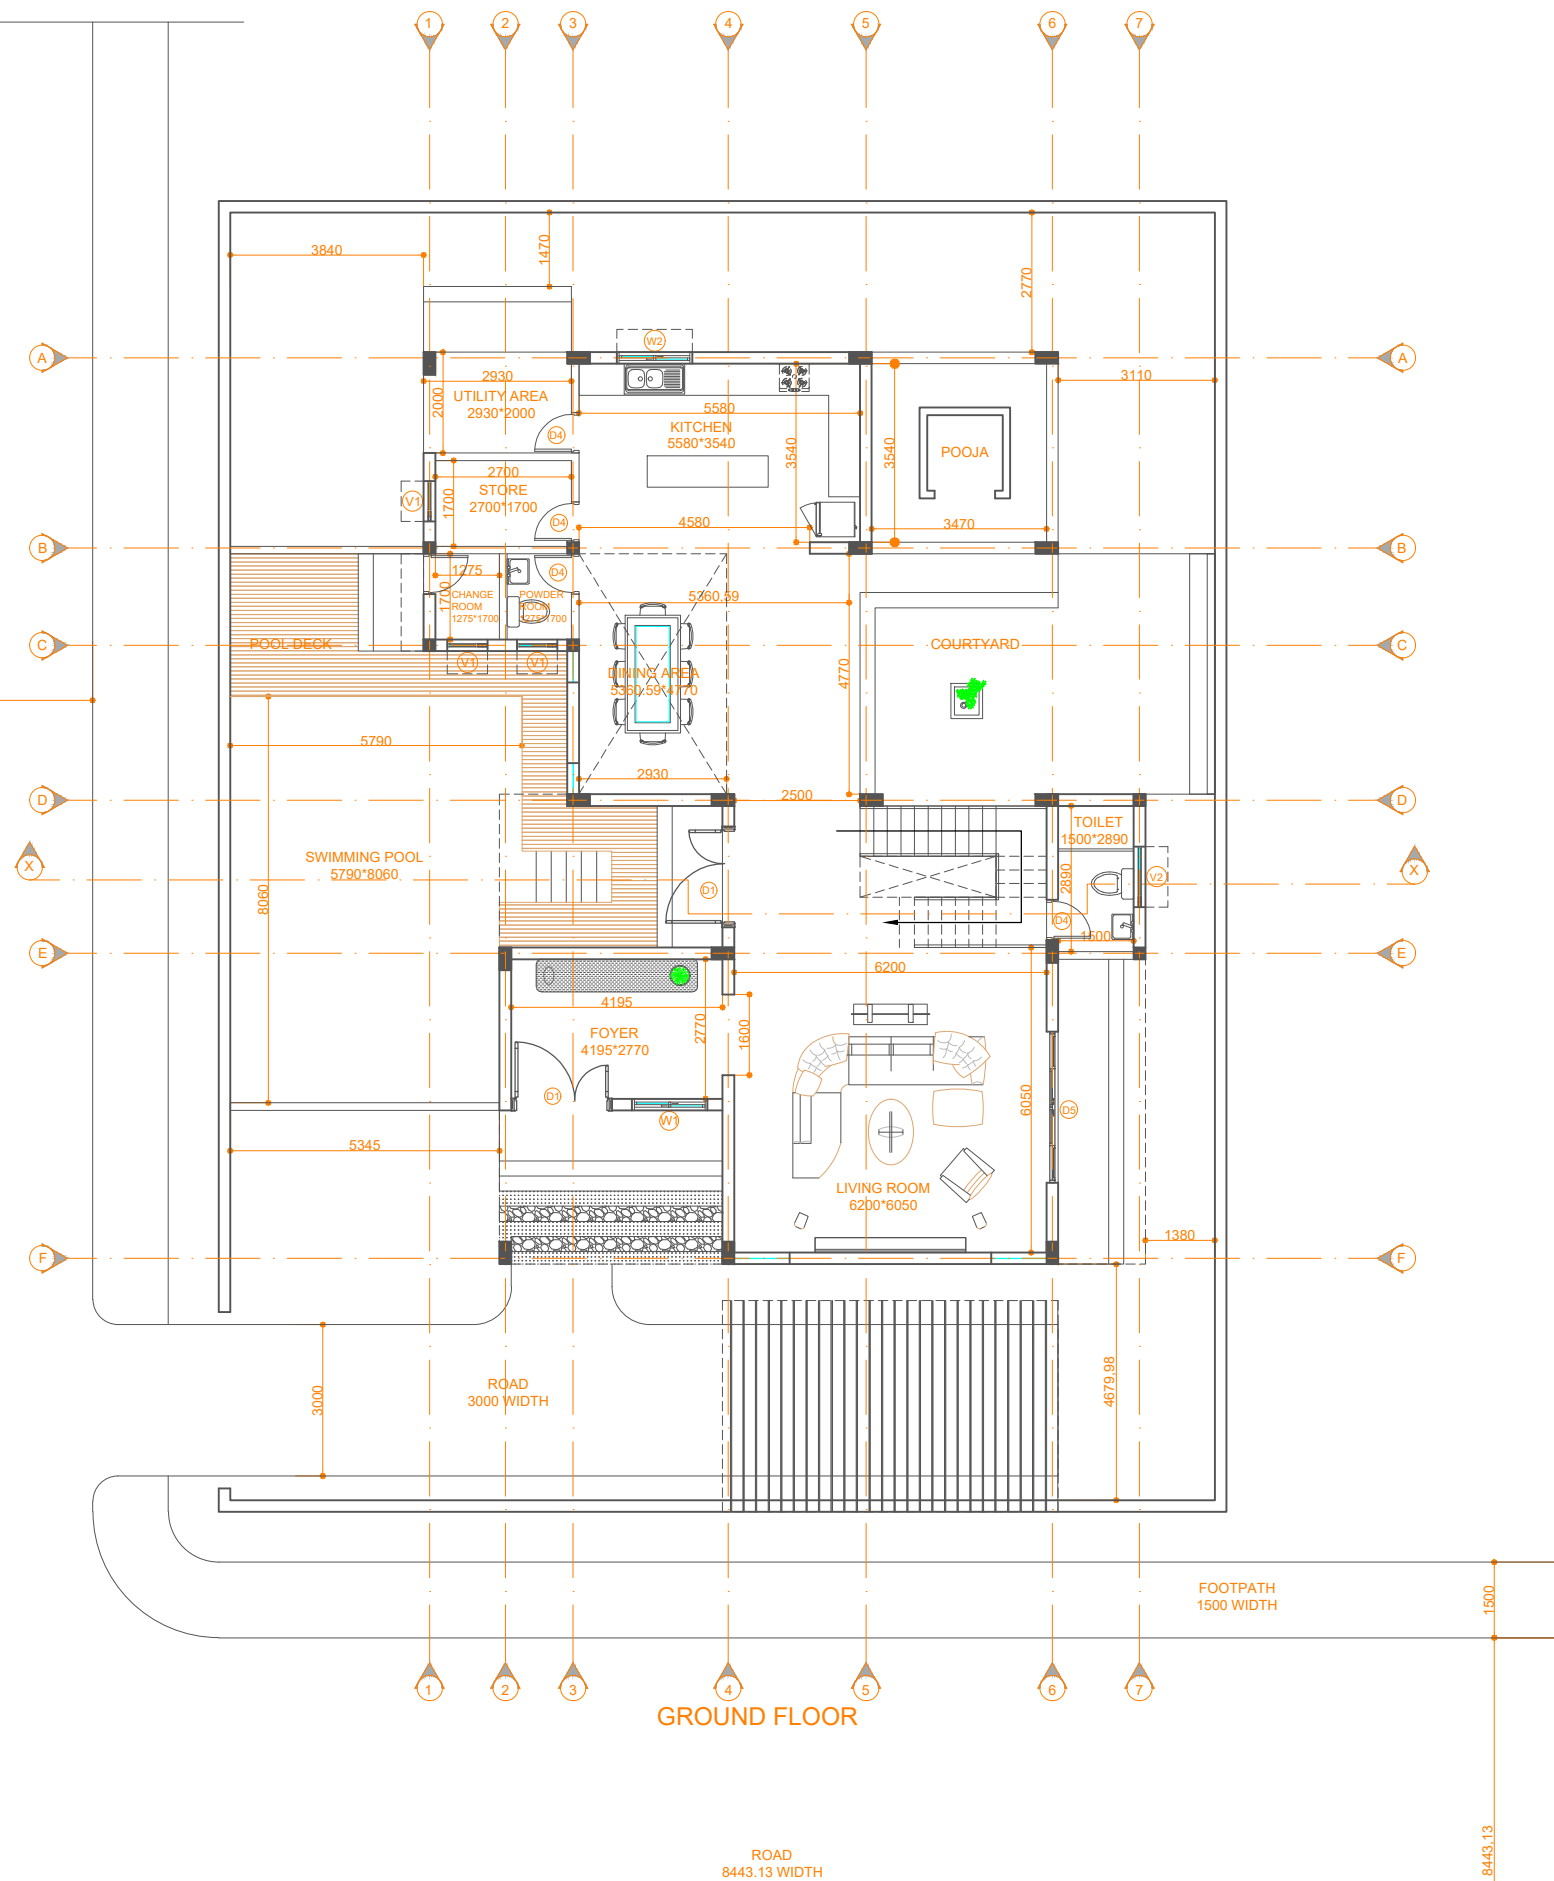

KEY PLAN

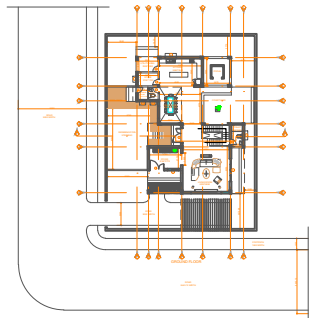

Notes:
1.While every attempt has been made in preparation of this drawing to avoid mistakes, the maker cannot guarantee against human error. The contractor on the job must check all dimensions and other details and be responsible for the same.
2.Unless otherwise mentioned all dimensions are in mm.
3.Written dimensions to be followed. Do not scale any measurement from the drawings.
4.Any discrepancy in this or any other drawings related to this drawing shall be brought to the notice of architects immediately.
5.This drawing is to be read in conjunction with related structural and services drawing.


IMPORTANT NOTE:

THIS IS THE PROPERTY OF ARTHAR ARCHITECTS GROUP & IS NOT TO BE COPIED, ISSUED, OR LOANED TO ANY THIRD PARTY FOR ANY PURPOSE OTHER THAN FOR WHICH IT HAS BEEN ISSUED.




DRAWING NAME: GROUND FLOOR PLAN

PROJECT TITLE:	VILLA HOUSE		
CLIENT NAME:	MS		
LOCATION:			
PLOT NO:		BLOCK NO:	
DESIGN BY:	KARAN	PROJECT NO:	
DRAWN BY:	KARAN	SHEET NO:	
CHECKED BY:		SCALE:	1:150
DRAWING NAME:	AR-01-MP-001-R00		

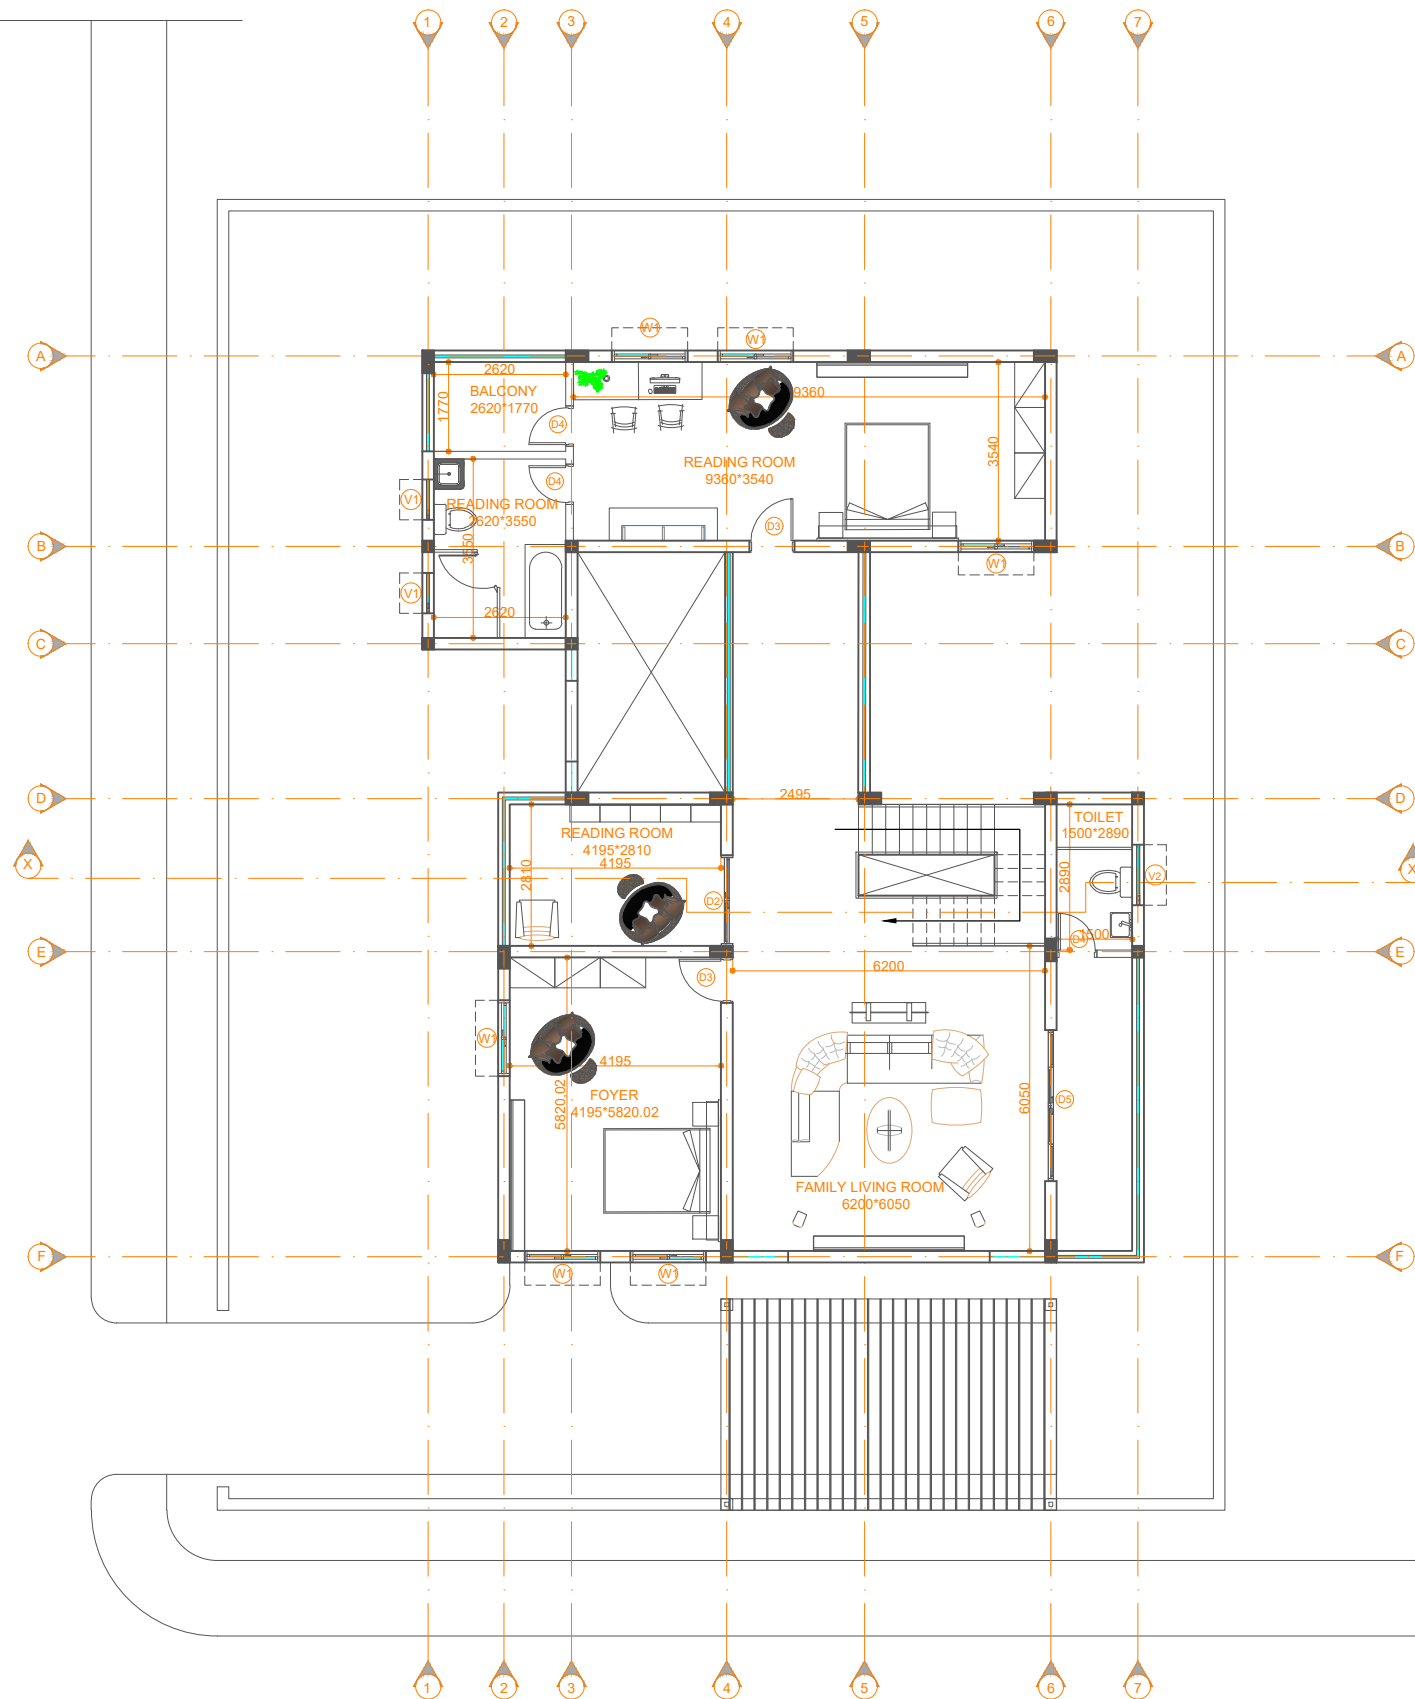

FIRST FLOOR PLAN

KEY PLAN

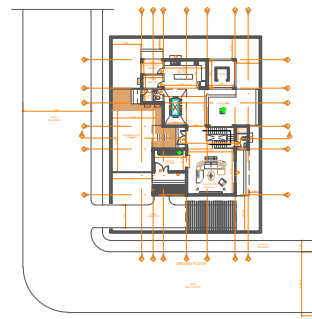

Notes:
1.While every attempt has been made in preparation of this drawing to avoid mistakes, the maker cannot guarantee against human error. The contractor on the job must check all dimensions and other details and be responsible for the same.
2.Unless otherwise mentioned all dimensions are in mm.
3.Written dimensions to be followed. Do not scale any measurement from the drawings.
4.Any discrepancy in this or any other drawings related to this drawing shall be brought to the notice of architects immediately.
5.This drawing is to be read in conjunction with related structural and services drawing.


IMPORTANT NOTE:

THIS IS THE PROPERTY OF ARTHAR ARCHITECTS GROUP & IS NOT TO BE COPIED, ISSUED, OR LOANED TO ANY THIRD PARTY FOR ANY PURPOSE OTHER THAN FOR WHICH IT HAS BEEN ISSUED.




DRAWING NAME: FIRST FLOOR PLAN

PROJECT TITLE:	VILLA HOUSE		
CLIENT NAME:	MS		
LOCATION:			
PLOT NO:		BLOCK NO:	
DESIGN BY:	KARAN	PROJECT NO:	
DRAWN BY:	KARAN	SHEET NO:	
CHECKED BY:		SCALE:	1:150
DRAWING NAME:	AR-01-MP-002-R00		

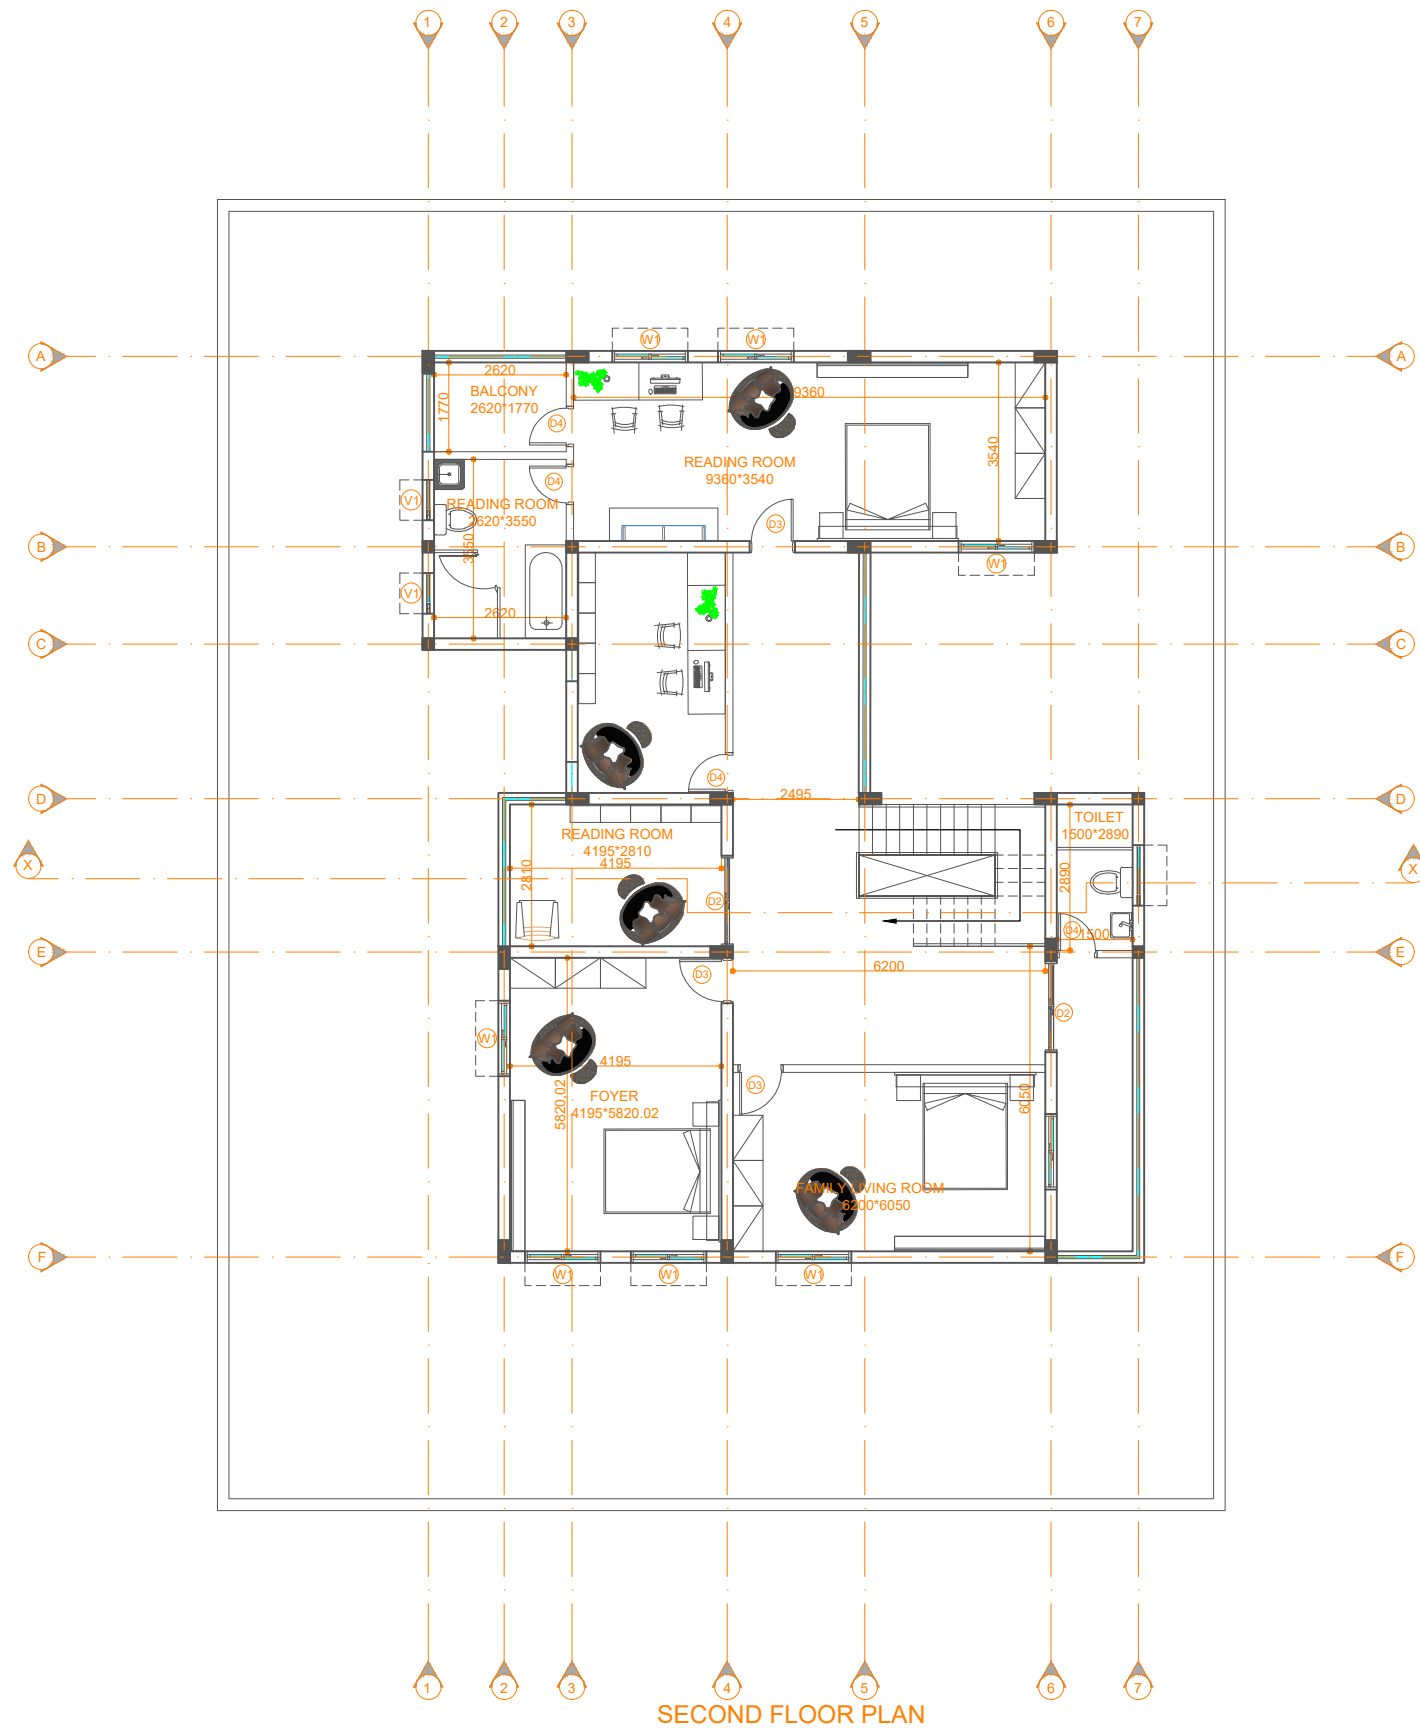

KEY PLAN

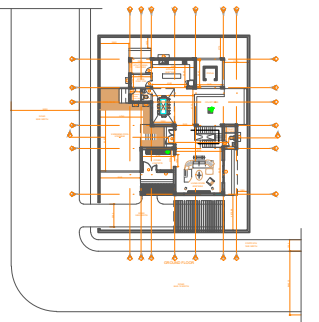

Notes:
1.While every attempt has been made in preparation of this drawing to avoid mistakes, the maker cannot guarantee against human error. The contractor on the job must check all dimensions and other details and be responsible for the same.
2.Unless otherwise mentioned all dimensions are in mm.
3.Written dimensions to be followed. Do not scale any measurement from the drawings.
4.Any discrepancy in this or any other drawings related to this drawing shall be brought to the notice of architects immediately.
5.This drawing is to be read in conjunction with related structural and services drawing.


IMPORTANT NOTE:

THIS IS THE PROPERTY OF ARTHAR ARCHITECTS GROUP & IS NOT TO BE COPIED, ISSUED, OR LOANED TO ANY THIRD PARTY FOR ANY PURPOSE OTHER THAN FOR WHICH IT HAS BEEN ISSUED.




DRAWING NAME: SECOND FLOOR PLAN

PROJECT TITLE:	VILLA HOUSE		
CLIENT NAME:	MS		
LOCATION:			
PLOT NO:		BLOCK NO:	
DESIGN BY:	KARAN	PROJECT NO:	
DRAWN BY:	KARAN	SHEET NO:	
CHECKED BY:		SCALE:	1:150
DRAWING NAME:	AR-01-MP-003-R00		

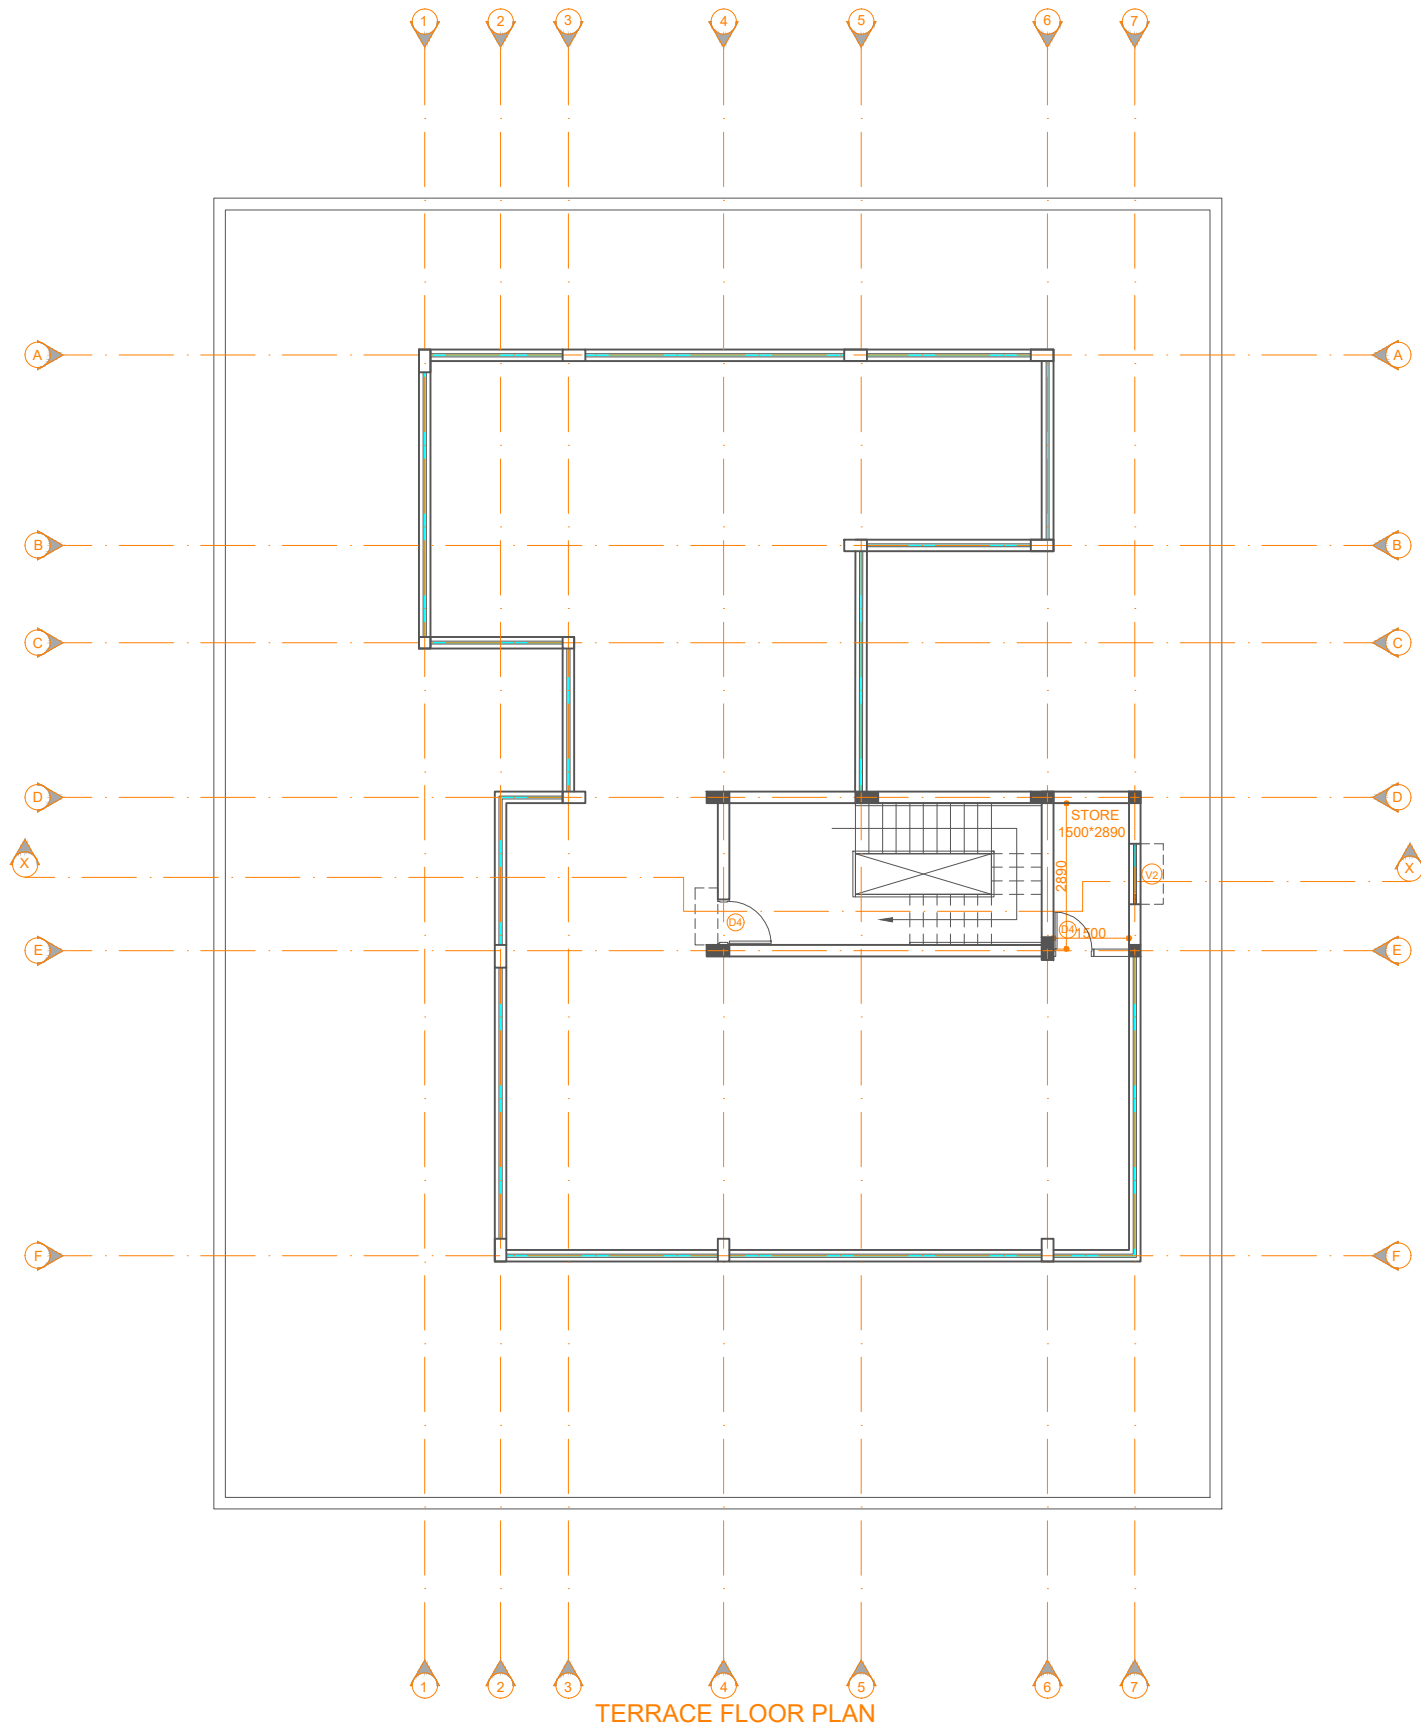

KEY PLAN

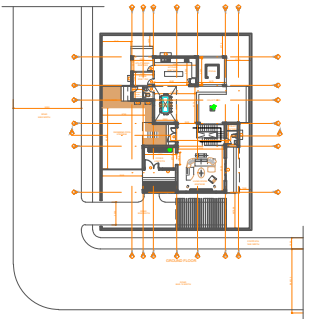

Notes:
1.While every attempt has been made in preparation of this drawing to avoid mistakes, the maker cannot guarantee against human error. The contractor on the job must check all dimensions and other details and be responsible for the same.
2.Unless otherwise mentioned all dimensions are in mm.
3.Written dimensions to be followed. Do not scale any measurement from the drawings.
4.Any discrepancy in this or any other drawings related to this drawing shall be brought to the notice of architects immediately.
5.This drawing is to be read in conjunction with related structural and services drawing.

IMPORTANT NOTE:

THIS IS THE PROPERTY OF ARTHA-R ARCHITECTS GROUP & IS NOT TO BE COPIED, ISSUED, OR LOANED TO ANY THIRD PARTY FOR ANY PURPOSE OTHER THAN FOR WHICH IT HAS BEEN ISSUED.



DRAWING NAME: TERRACE PLAN

PROJECT TITLE: VILLA HOUSE

CLIENT NAME: MS

LOCATION:

PLOT NO:

BLOCK NO:

DESIGN BY:

KARAN

PROJECT NO:

DRAWN BY:

KARAN

SHEET NO:


CHECKED BY:

SCALE:

1:150


DRAWING NAME:

AR-01-MP-004-R00

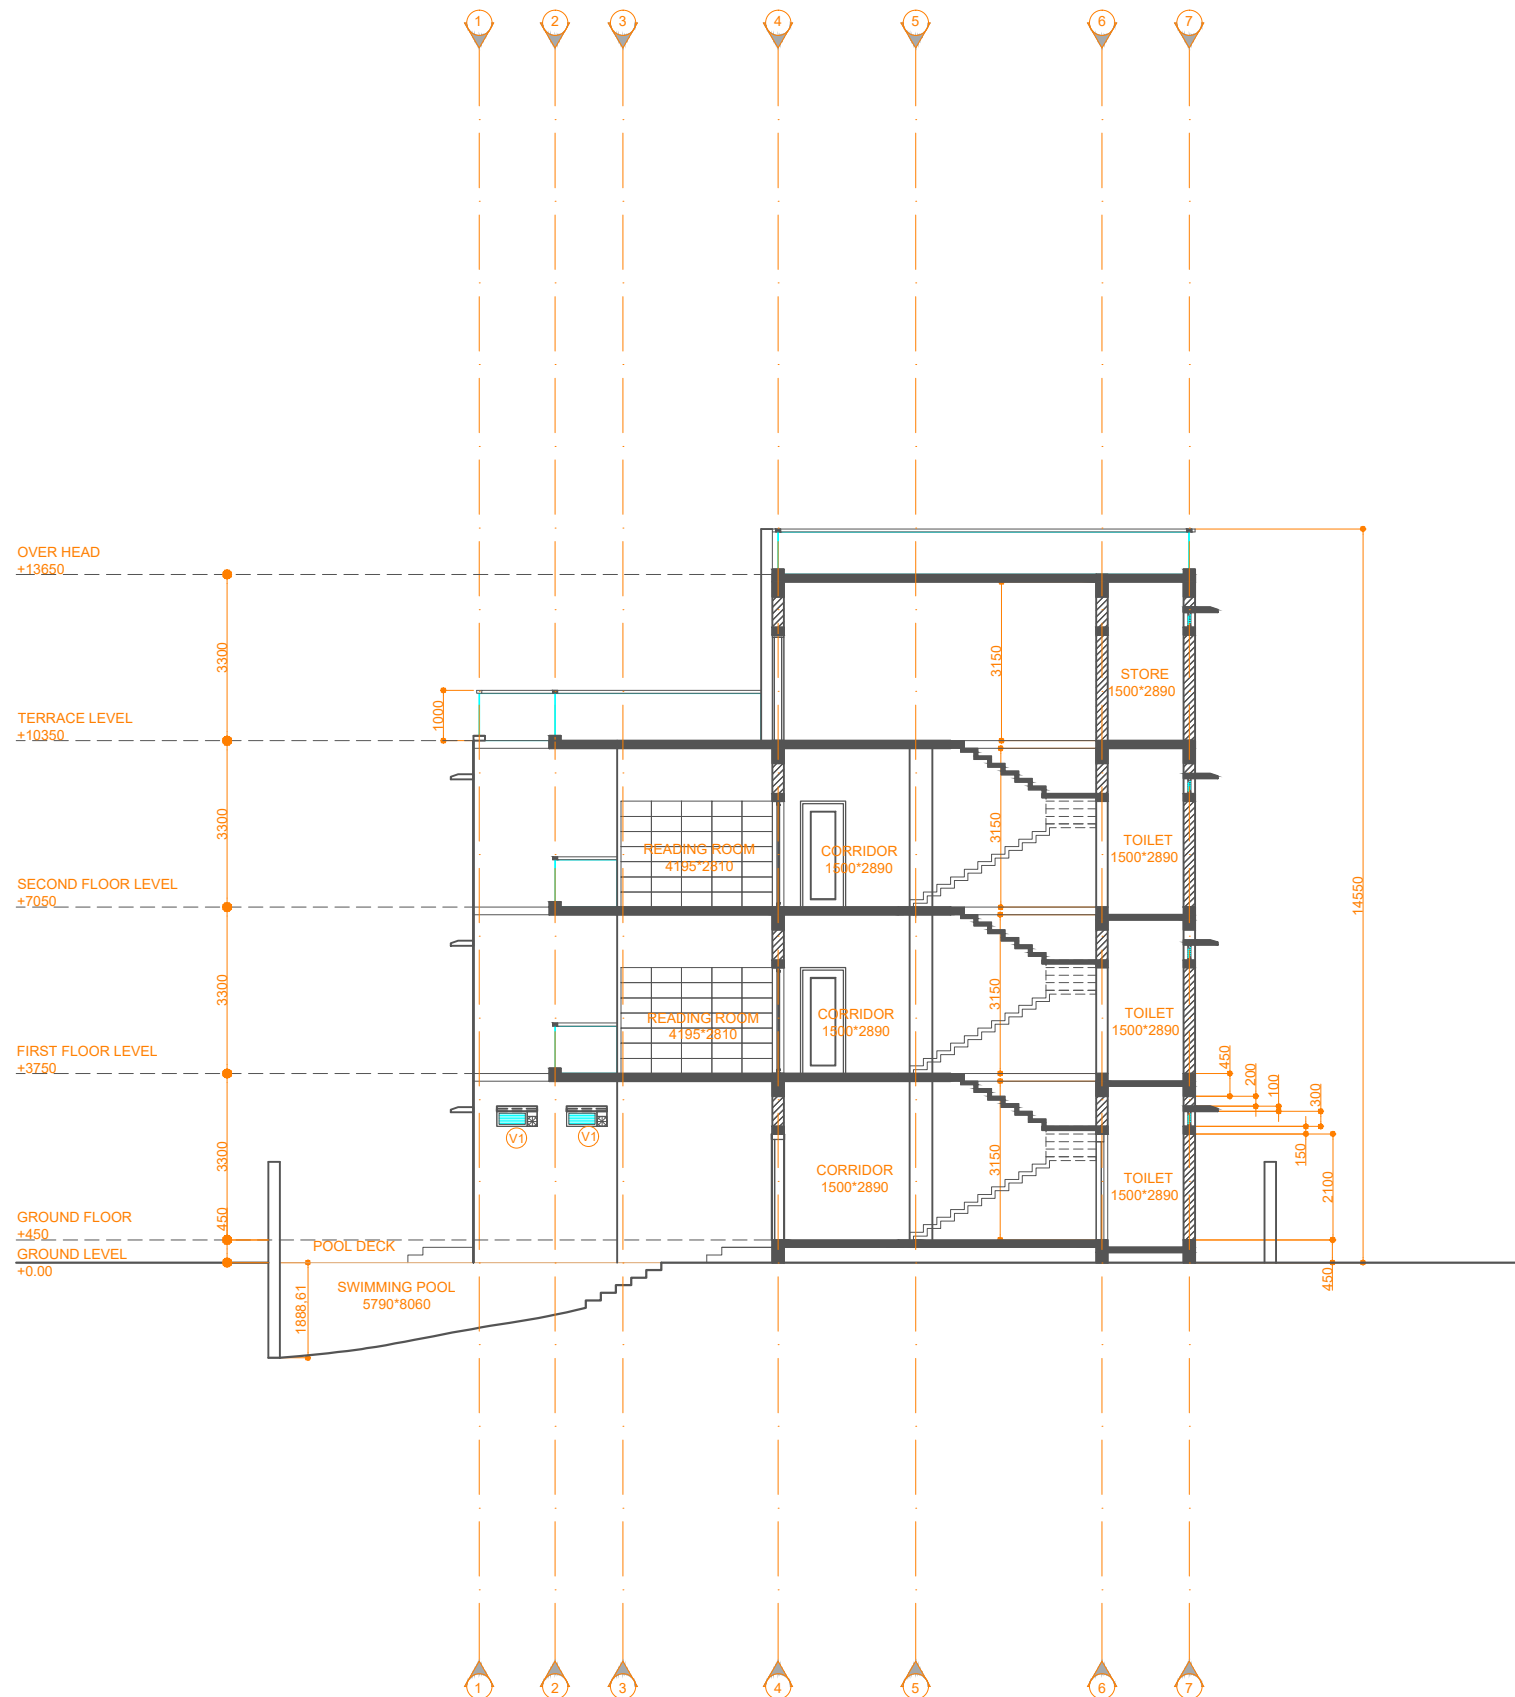

SECTION AT XX

KEY PLAN

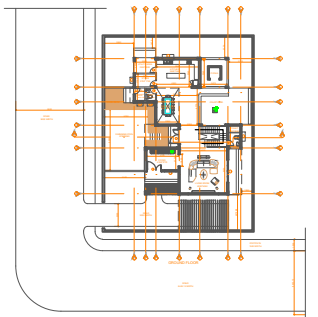

Notes:
1.While every attempt has been made in preparation of this drawing to avoid mistakes, the maker cannot guarantee against human error. The contractor on the job must check all dimensions and other details and be responsible for the same.
2.Unless otherwise mentioned all dimensions are in mm.
3.Written dimensions to be followed. Do not scale any measurement from the drawings.
4.Any discrepancy in this or any other drawings related to this drawing shall be brought to the notice of architects immediately.
5.This drawing is to be read in conjunction with related structural and services drawing.



IMPORTANT NOTE:

THIS IS THE PROPERTY OF ARTHA R ARCHITECTS GROUP & IS NOT TO BE COPIED, ISSUED, OR LOANED TO ANY THIRD PARTY FOR ANY PURPOSE OTHER THAN FOR WHICH IT HAS BEEN ISSUED.




DRAWING NAME: SECTION

PROJECT TITLE:	VILLA HOUSE		
CLIENT NAME:	MS		
LOCATION:			
PLOT NO:		BLOCK NO:	
DESIGN BY:	KARAN	PROJECT NO:	
DRAWN BY:	KARAN	SHEET NO:	
CHECKED BY:		SCALE:	1:150
DRAWING NAME:	AR-01-SE-001-R00		

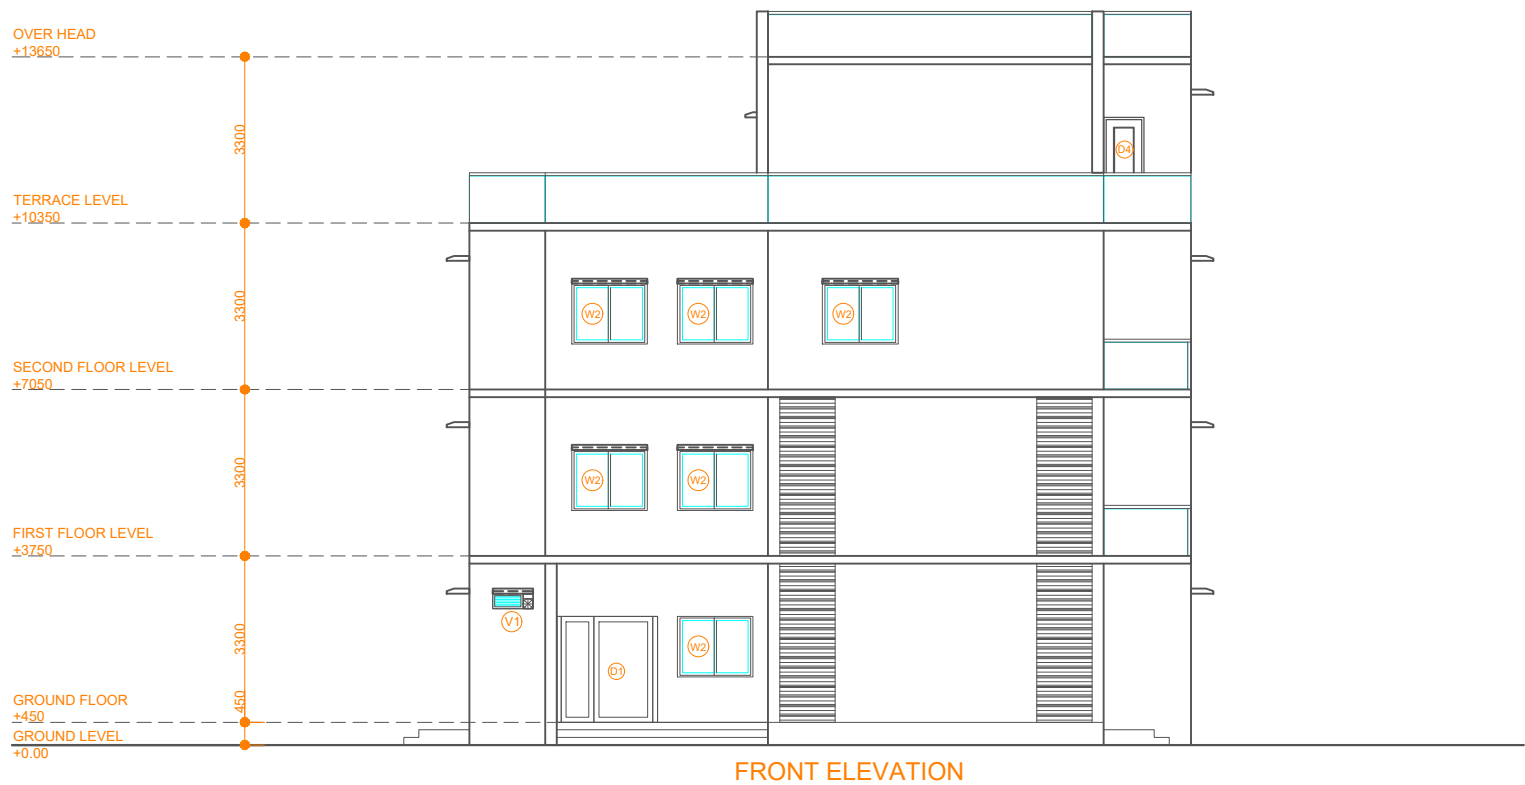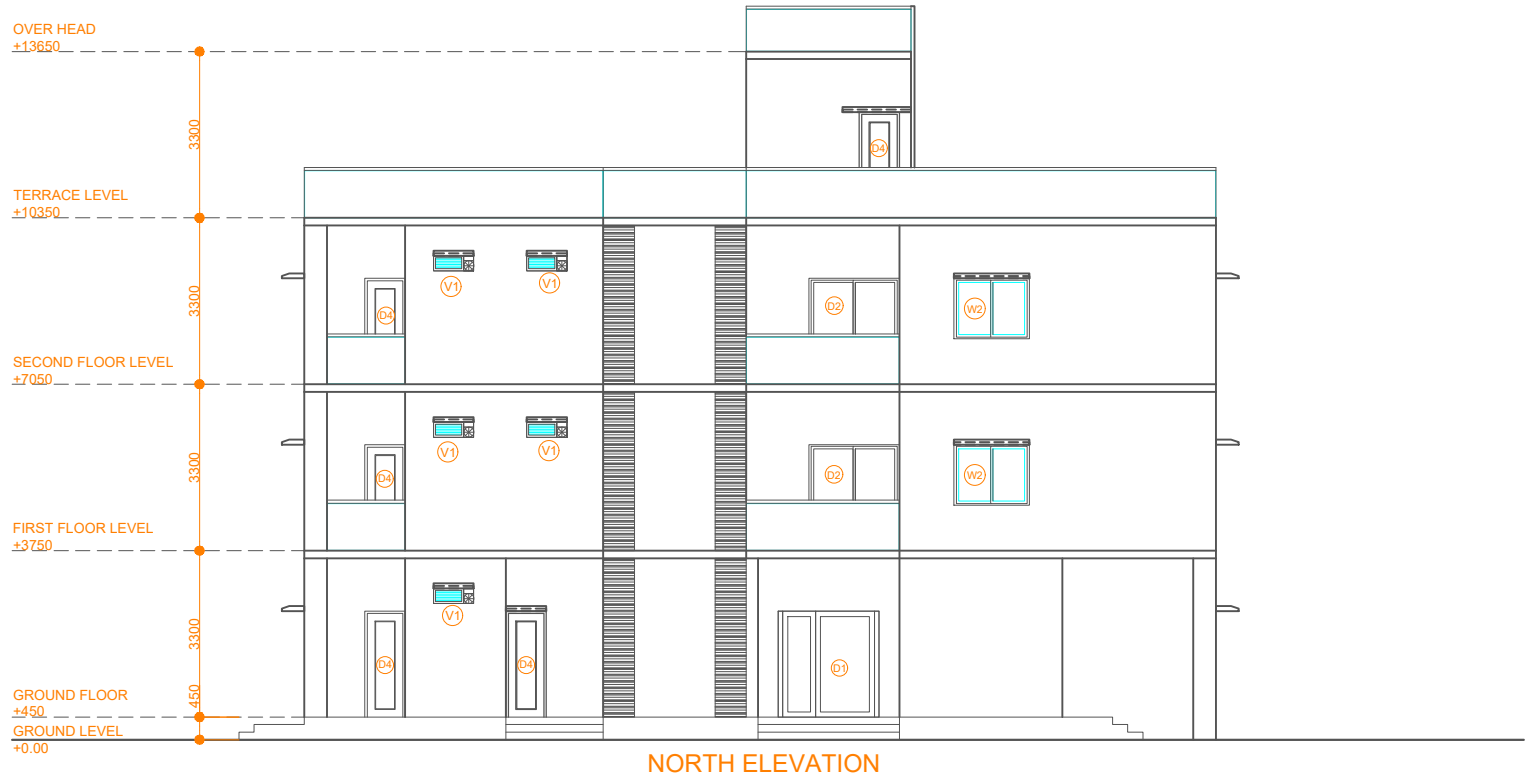

KEY PLAN

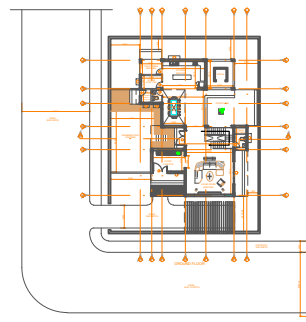

Notes:

- 1.While every attempt has been made in preparation of this drawing to avoid mistakes, the maker cannot guarantee against human error. The contractor on the job must check all dimensions and other details and be responsible for the same.
- 2.Unless otherwise mentioned all dimensions are in mm.
- 3.Written dimensions to be followed. Do not scale any measurement from the drawings.
- 4.Any discrepancy in this or any other drawings related to this drawing shall be brought to the notice of architects immediately.
- 5.This drawing is to be read in conjunction with related structural and services drawing.




IMPORTANT NOTE:

THIS IS THE PROPERTY OF ARTHA-R ARCHITECTS GROUP & IS NOT TO BE COPIED, ISSUED, OR LOANED TO ANY THIRD PARTY FOR ANY PURPOSE OTHER THAN FOR WHICH IT HAS BEEN ISSUED.




DRAWING NAME: ELEVATION

PROJECT TITLE:	VILLA HOUSE		
CLIENT NAME:	MS		
LOCATION:			
PLOT NO:		BLOCK NO:	
DESIGN BY:	KARAN	PROJECT NO:	
DRAWN BY:	KARAN	SHEET NO:	
CHECKED BY:		SCALE:	1:150
DRAWING NAME:	AR-01-EL-001-R00		

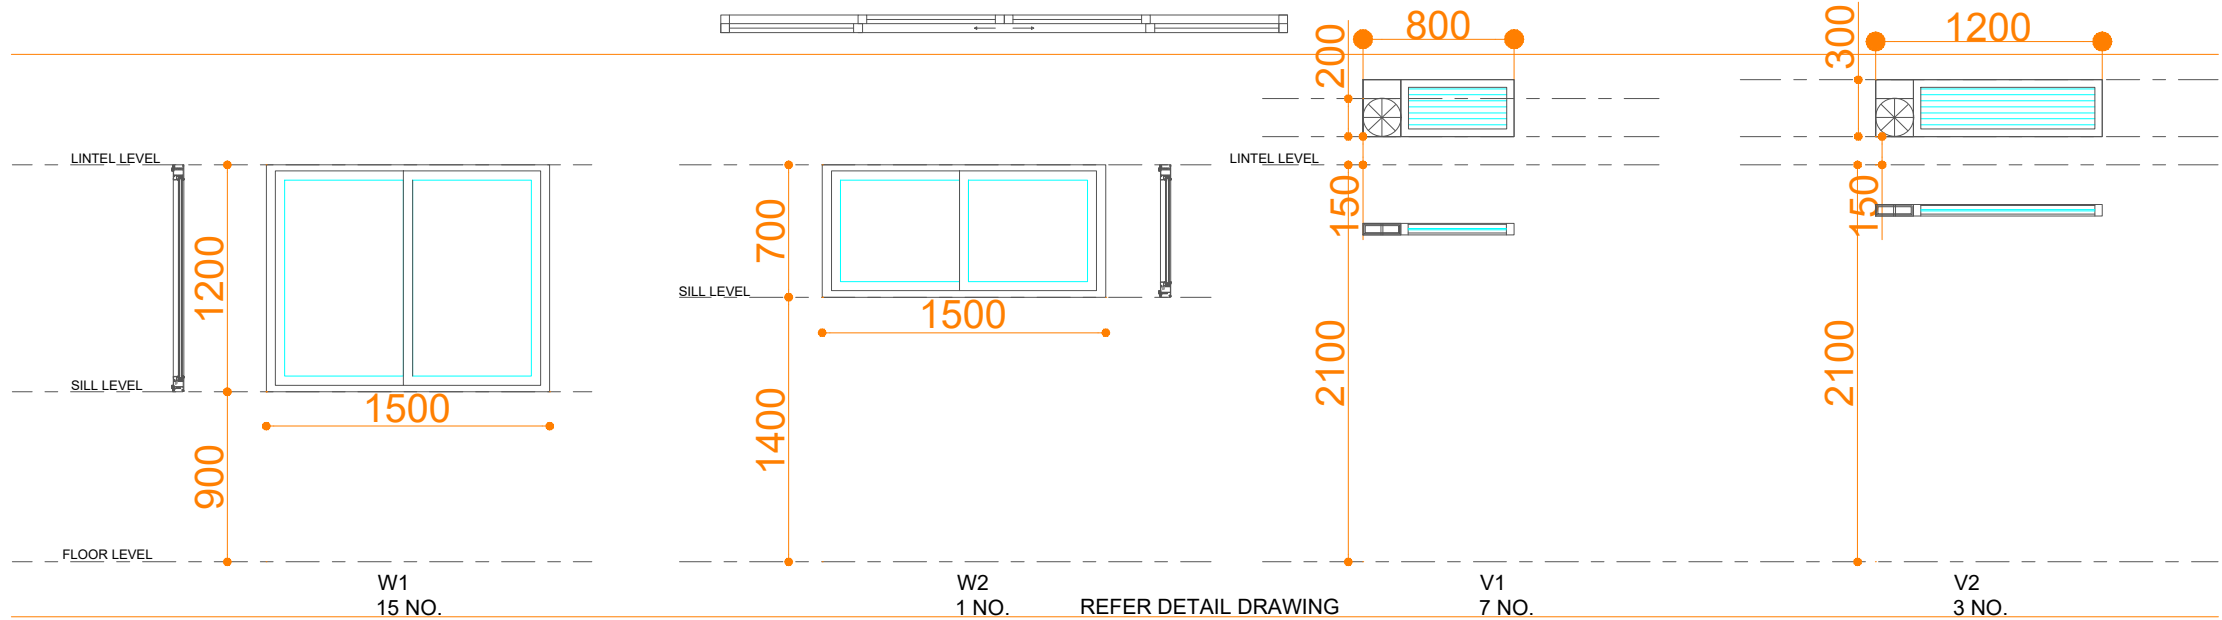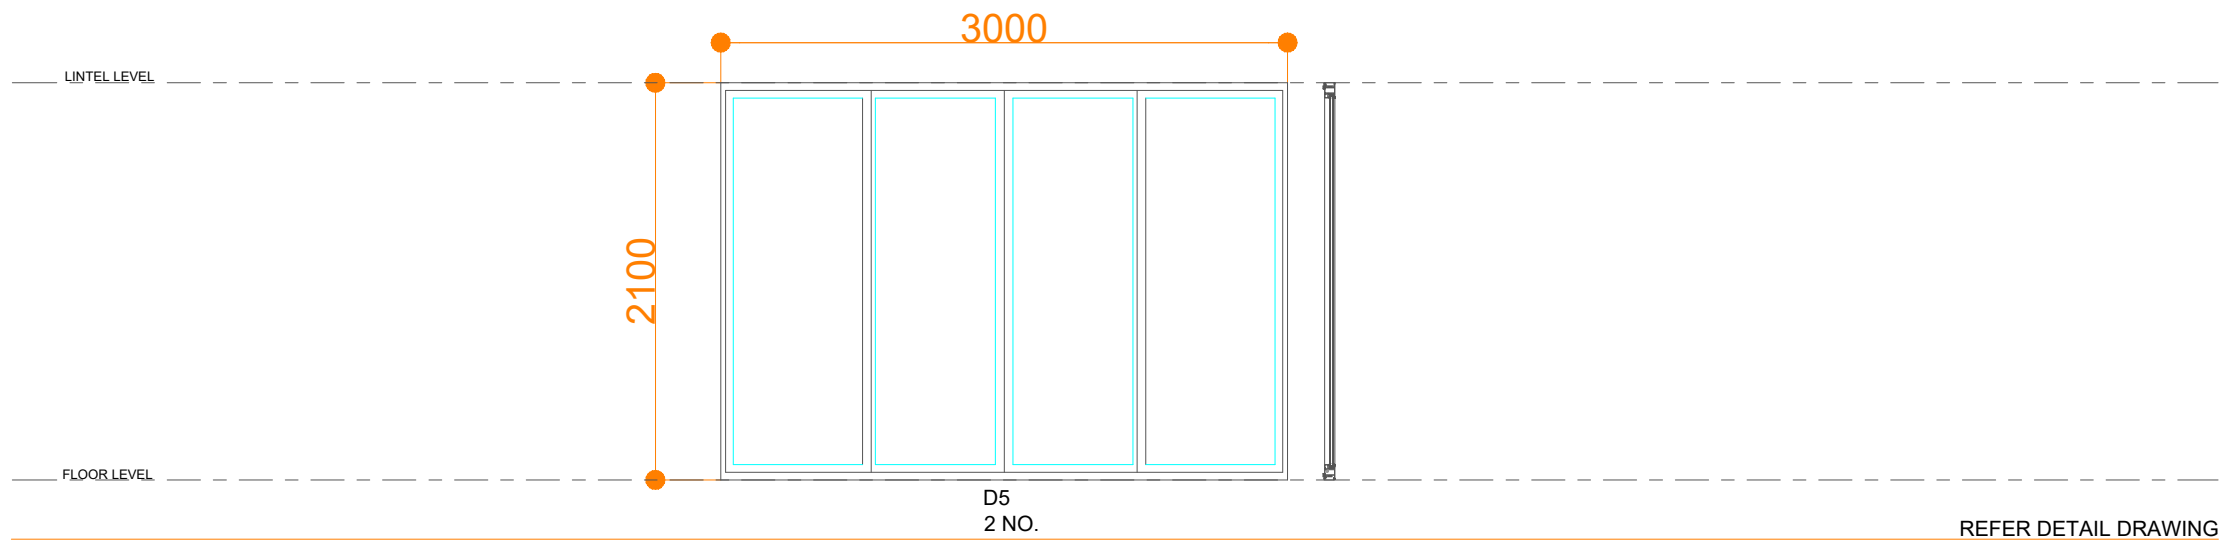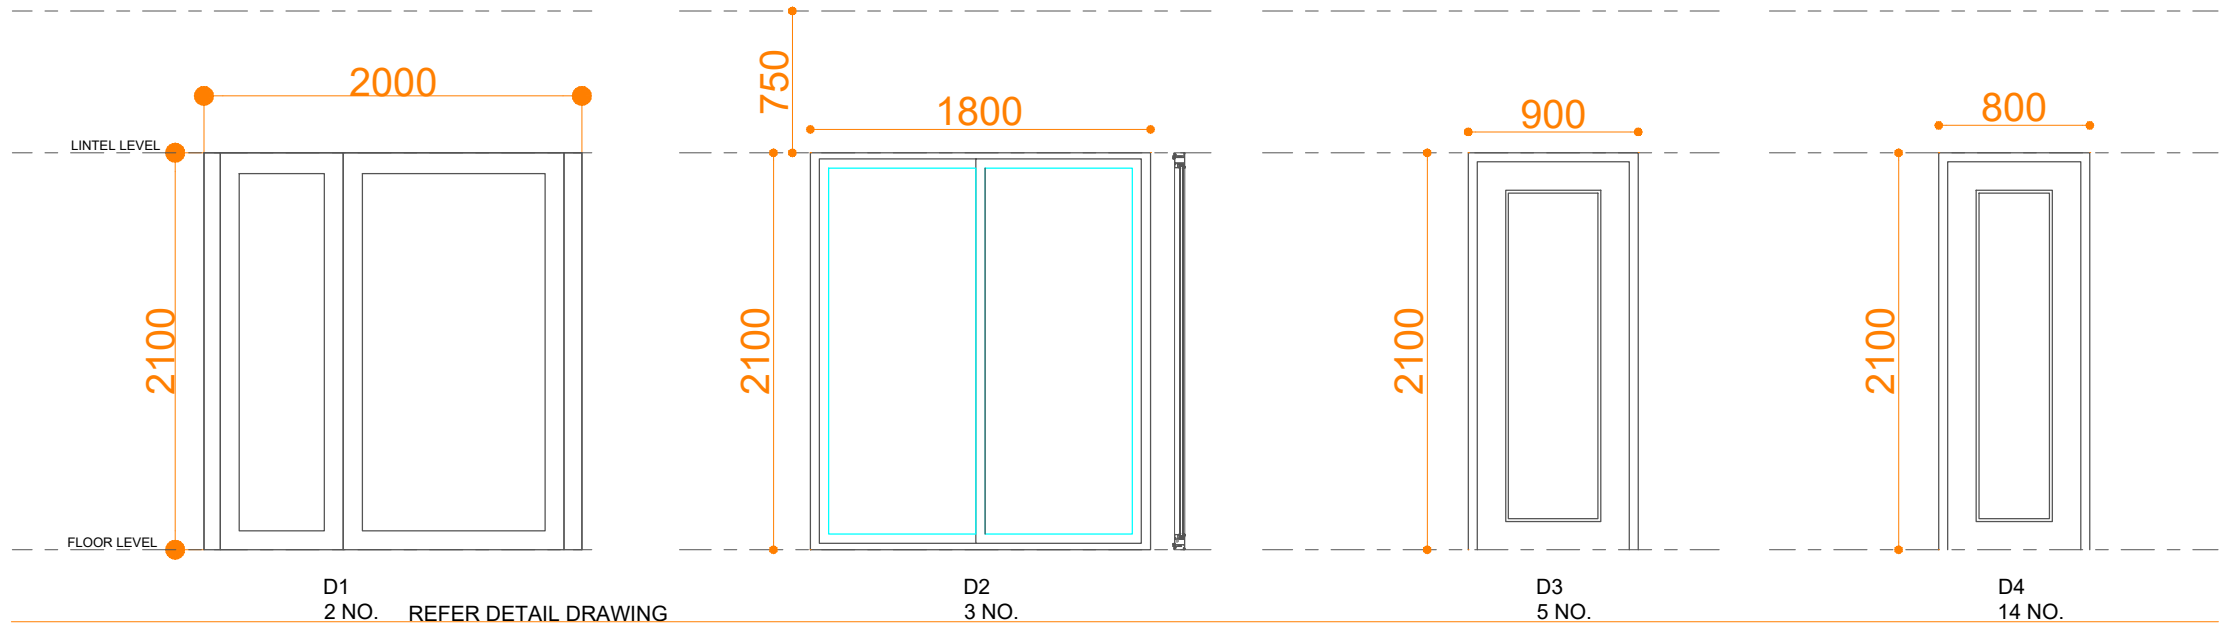

KEY PLAN

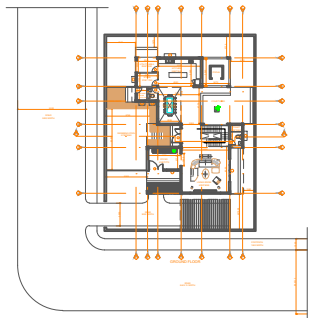

Notes:
1.While every attempt has been made in preparation of this drawing to avoid mistakes, the maker cannot guarantee against human error. The contractor on the job must check all dimensions and other details and be responsible for the same.
2.Unless otherwise mentioned all dimensions are in mm.
3.Written dimensions to be followed. Do not scale any measurement from the drawings.
4.Any discrepancy in this or any other drawings related to this drawing shall be brought to the notice of architects immediately.
5.This drawing is to be read in conjunction with related structural and services drawing.





IMPORTANT NOTE:

THIS IS THE PROPERTY OF ARTHA R ARCHITECTS GROUP & IS NOT TO BE COPIED, ISSUED, OR LOANED TO ANY THIRD PARTY FOR ANY PURPOSE OTHER THAN FOR WHICH IT HAS BEEN ISSUED.



DRAWING NAME: DOOR-WINDOW SHEDULE

PROJECT TITLE:	VILLA HOUSE		
CLIENT NAME:	MS		
LOCATION:			
PLOT NO:		BLOCK NO:	
DESIGN BY:	KARAN	PROJECT NO:	
DRAWN BY:	KARAN	SHEET NO:	
CHECKED BY:		SCALE:	1:40
DRAWING NAME:	AR-01-DW-001-R00		

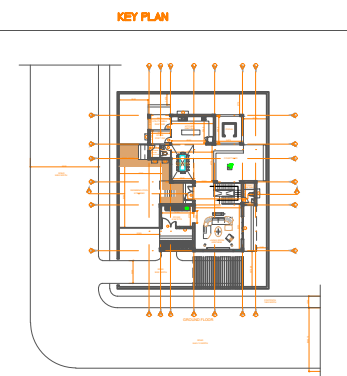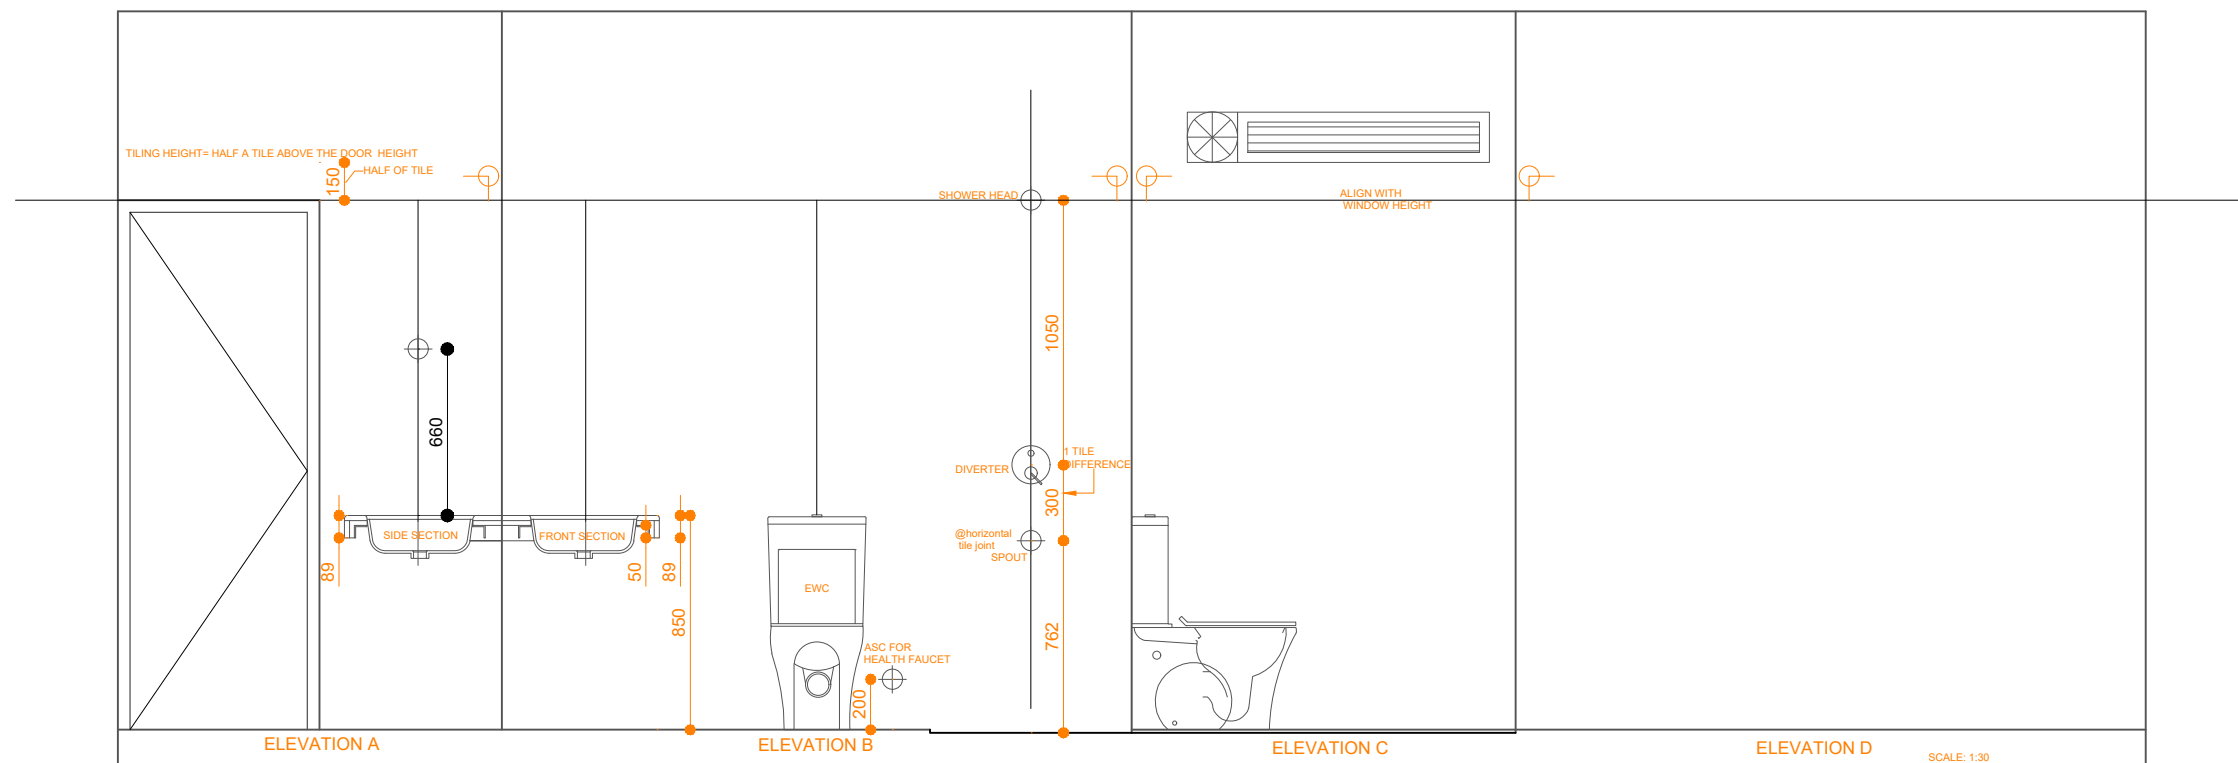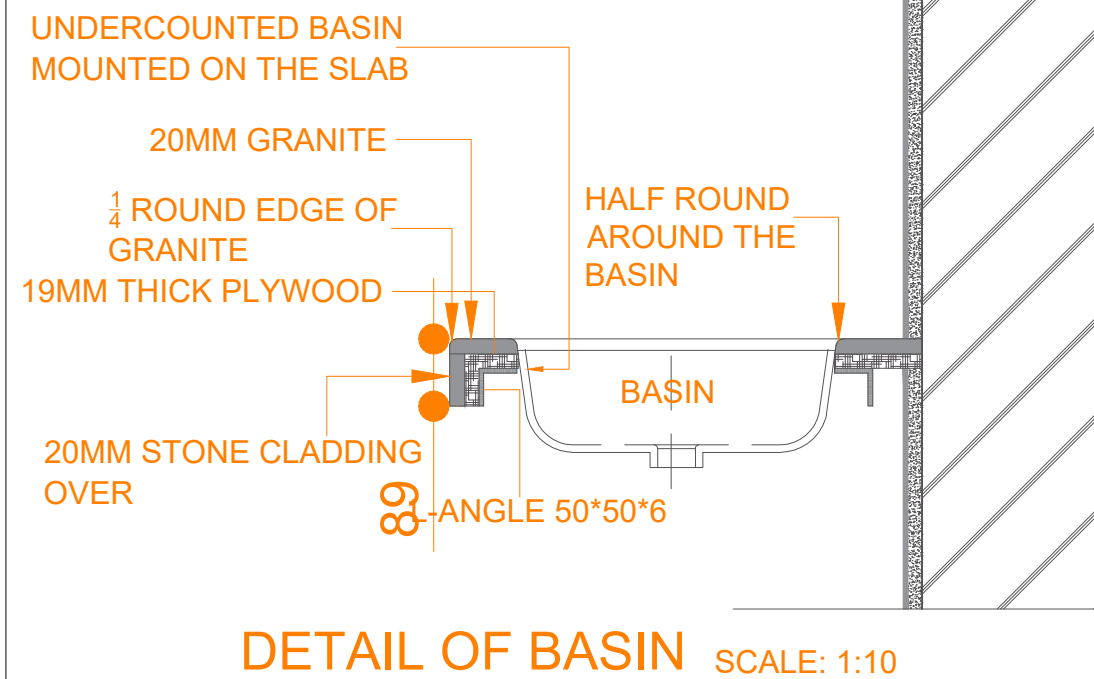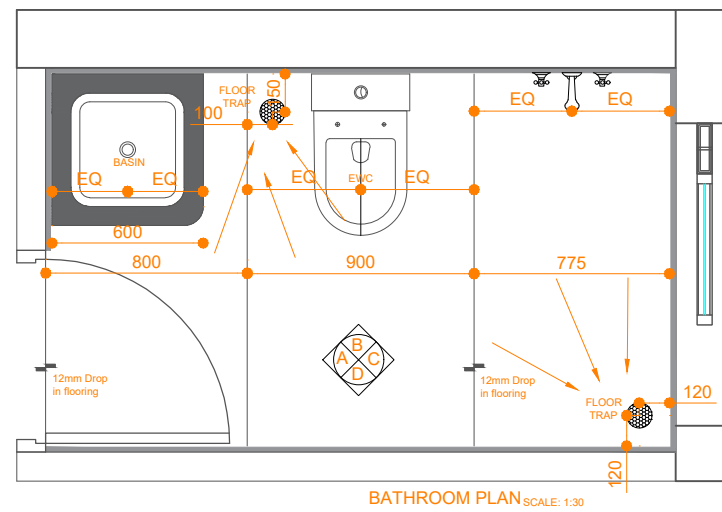

Notes:

1. While every attempt has been made in preparation of this drawing to avoid mistakes, the maker cannot guarantee against human error. The contractor on the job must check all dimensions and other details and be responsible for the same.
2. Unless otherwise mentioned all dimensions are in mm.
3. Written dimensions to be followed. Do not scale any measurement from the drawings.
4. Any discrepancy in this or any other drawings related to this drawing shall be brought to the notice of architects immediately.
5. This drawing is to be read in conjunction with related structural and services drawing.

IMPORTANT NOTE:

THIS IS THE PROPERTY OF ARTHA.R ARCHITECTS GROUP & IS NOT TO BE COPIED, ISSUED, OR LOANED TO ANY THIRD PARTY FOR ANY PURPOSE OTHER THAN FOR WHICH IT HAS BEEN ISSUED.



DRAWING NAME: TOILET DETAIL

PROJECT TITLE:		VILLA HOUSE	
CLIENT NAME:		MS	
LOCATION:			
PLOT NO:		BLOCK NO:	
DESIGN BY:	KARAN	PROJECT NO:	
DRAWN BY:	KARAN	SHEET NO:	
CHECKED BY:		SCALE:	1:30
DRAWING NAME:		AR-01-DD-001-R00	